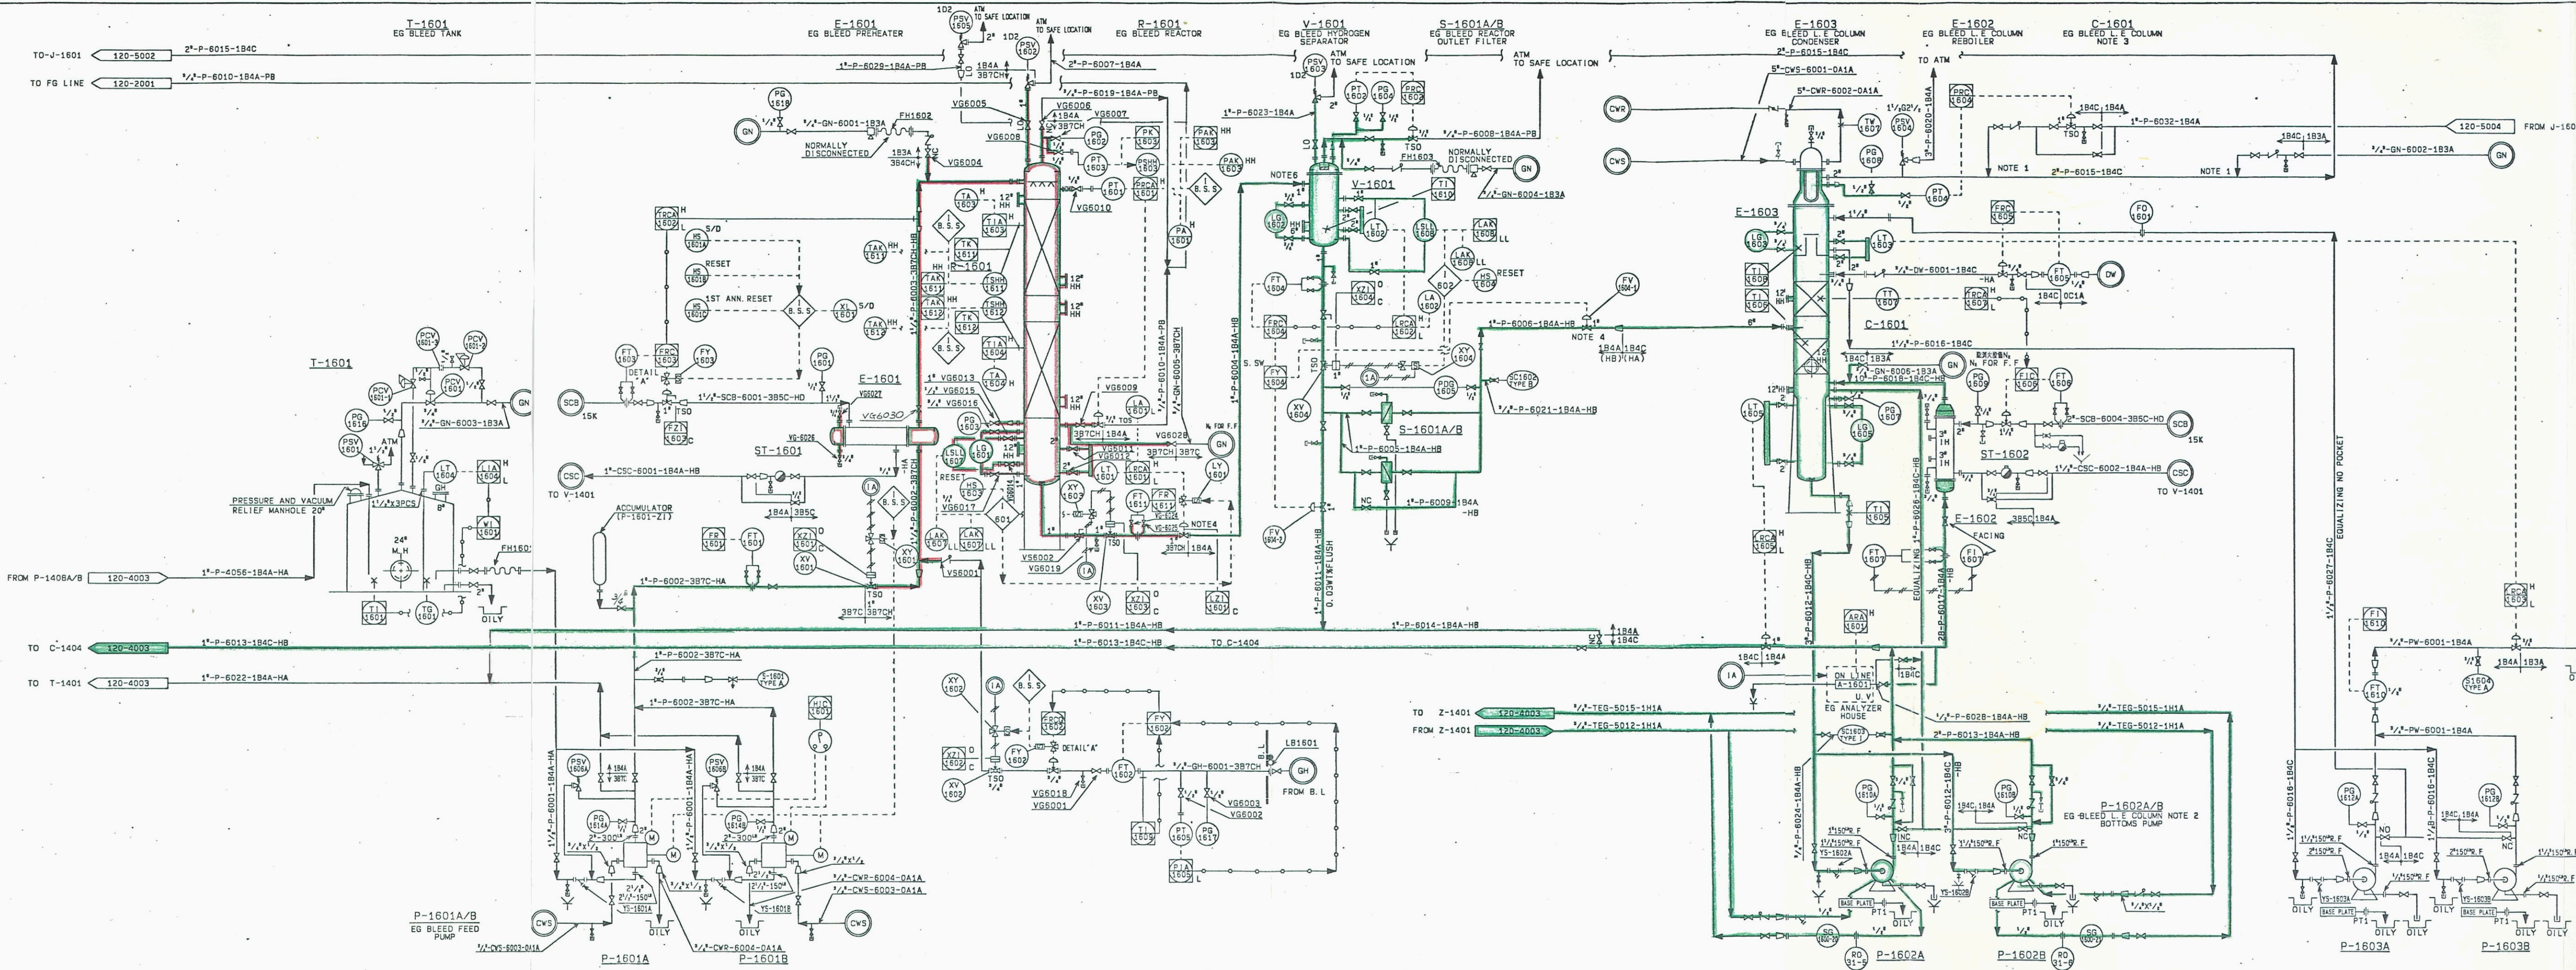


- NOTES
1. NITROGEN INJECTION POINT MUST BE ON TOP OF LINE TO VACUUM SYSTEM.
 2. DOUBLE MECHANICAL SEALS TO BE USED ON ALL PUMPS OPERATING ON VACUUM EQUIPMENT.
 3. DESIGN VACUUM COLUMNS AND ACCESSORIES FOR MINIMUM AIR LEAKAGE.
 4. PROCESS STREAM FLASHES ACROSS VALVE LOCATE NEAR INLET OF DOWN STREAM COLUMN.
 5. LOCATE NOZZLE OF THE VESSEL TANGENTIALLY.
 6. MINIMUM NOZZLE SIZE ON EQUIPMENT SHALL BE 1/2".

P&ID NO.		REV. NO.	
120-6001		03-14-06-01	
PROJECT		CUSTOMER	
MPC/MEPC		KGC7 03' 12'	
SECTION		PROJECT	
M. KARASAKI		UNIT 1600 ED BLEED RECOVERY (MYKK PROCESS) UNIT	
CHECKED		DWN. NO.	
M. TERAMOTO		3444 B240-01200	
DATE		SCALE	
OCT. 17 '80			